
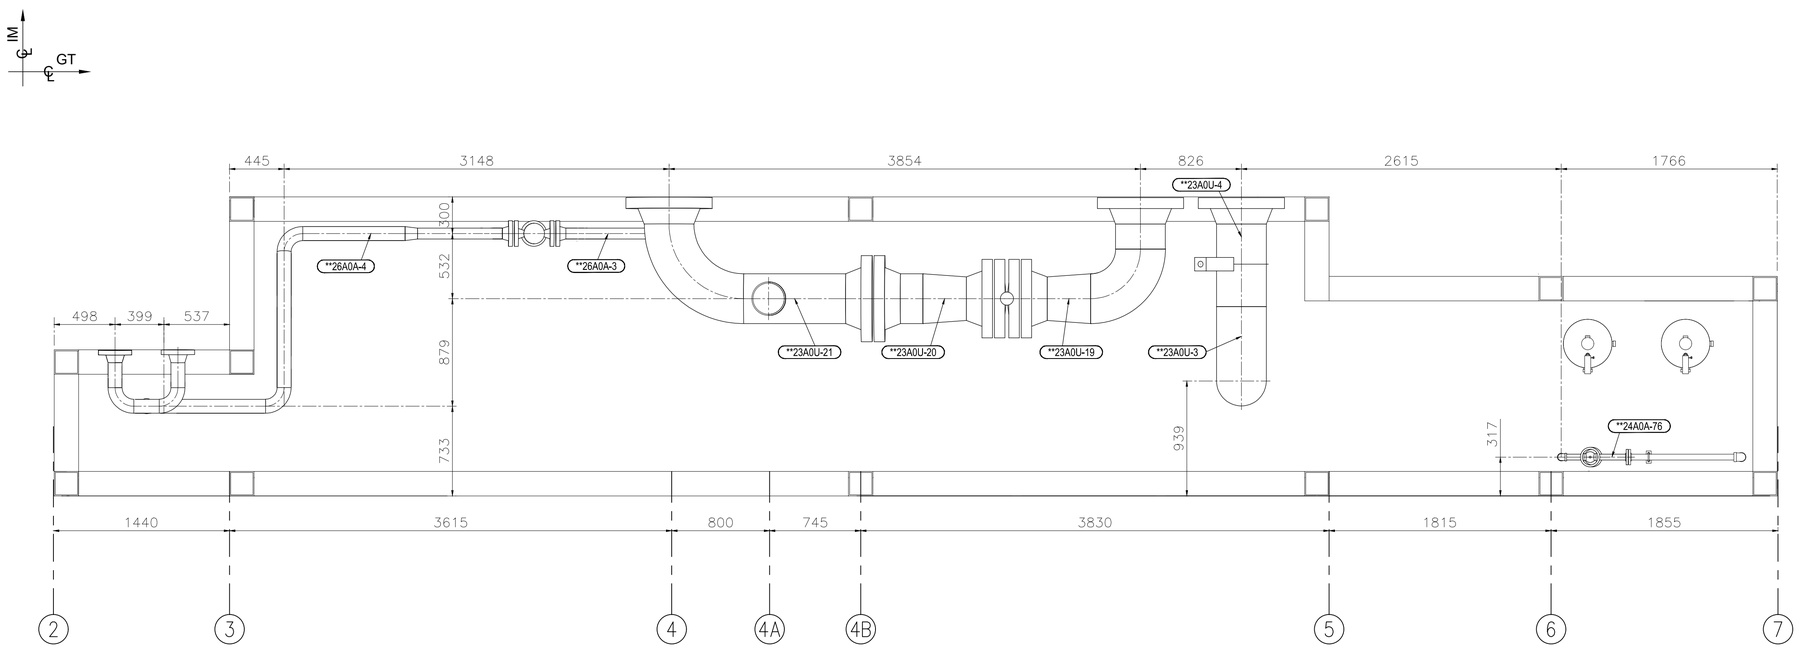


MD-3.1 PLAN VIEW
SECTION 'A-A'

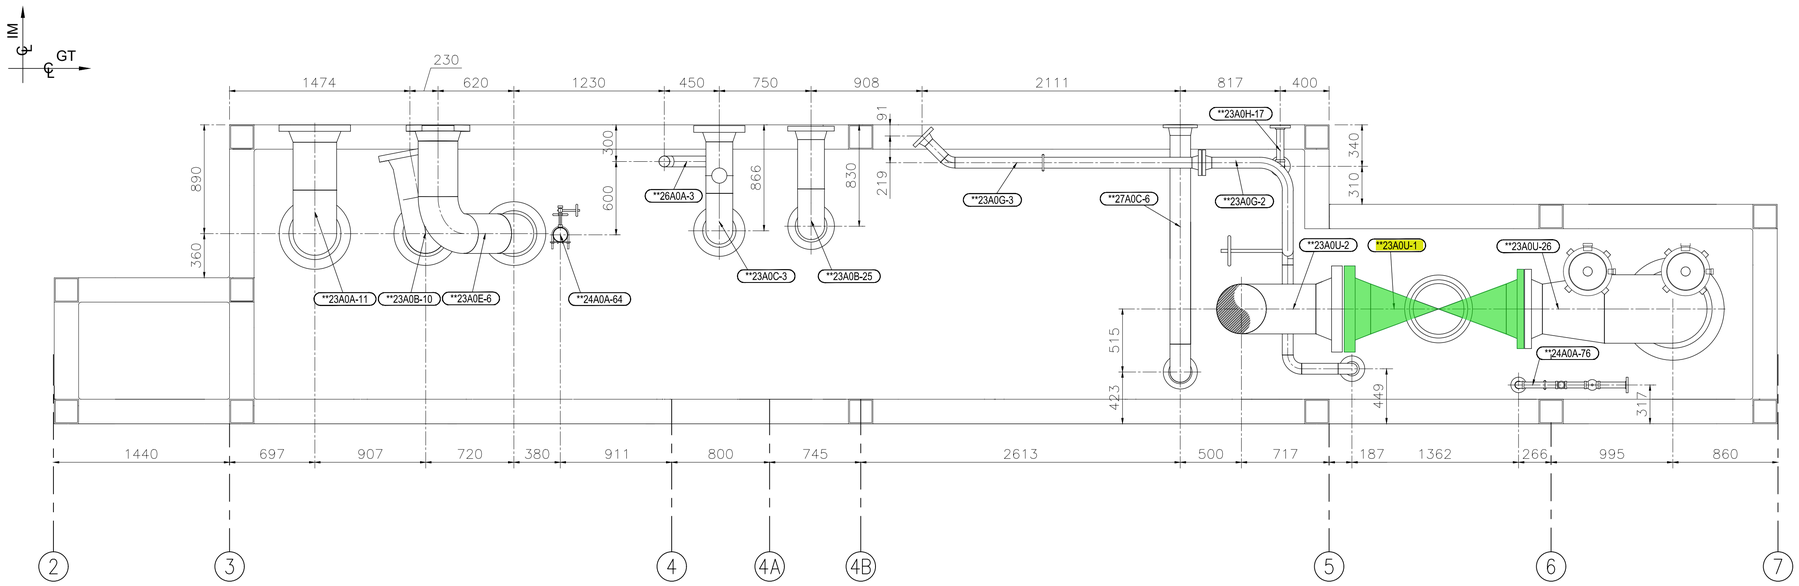

MD-3.1 PLAN VIEW
SECTION 'B-B'

REFERENCES

MDL ITEM #	MPWA MDL DESCRIPTION	DETAILS FOR
1	FOUNDATION PLAN AND SUMMARY LOADING DATA FOR MODULE GT ENCLOSURE	GENERAL LOCATION
20	GA DRAWING FOR MODULARIZED JAC GT ENCLOSURE	GENERAL LOCATION

NOTES

1. DIMENSIONS : MM [INCHES]
2. LABELING
   - **XXXXXX —— PIPE LINE
   - (**XXX-X) —— SPOOL NO
3. SOME STRUCTURAL MEMBERS AND GRATINGS ARE HIDDEN FOR A MORE CLEAR VIEW WHERE IT IS CONSIDERED NECESSARY
4. WP : WORKING POINT FOR SLOPE LINE

REV.	DESCRIPTION	DATE	BY	CHECK	APPROVAL
0	ISSUED FOR CONSTRUCTION	01.MAY.2024	S.H.	M.F.	N.K.

This drawing is the property of Cimtas and all rights reserved

REVISIONS

CUSTOMER

PROPRIETARY AND CONFIDENTIAL:
This document contains Confidential and Proprietary information of Mitsubishi Power Americas, Inc. Neither this document, nor any information obtained therefrom is to be reproduced, transmitted or disclosed to any third party without first receiving the express written authorization of Mitsubishi Power Americas, Inc.
©2024 , Mitsubishi Power Americas, Inc.

MITSUBISHI POWER

CUSTOMER JOB NO: –

ITEM NO: MDL-150

DWG NAME: MD-3.1 PIPING SUPPORT & SPOOLS GENERAL ARRANGEMENTS DRAWINGS **(GA FOR SPOOLS)**


REF.DWG.NO.: –

PREPARED BY: cimtas


JOB NO	SHEET	SCALE	SIZE
2E00140	1/1	1/25	A1

DRAWING NO: 2E00140-PI-094-001-MD-3.1


REV.: 0

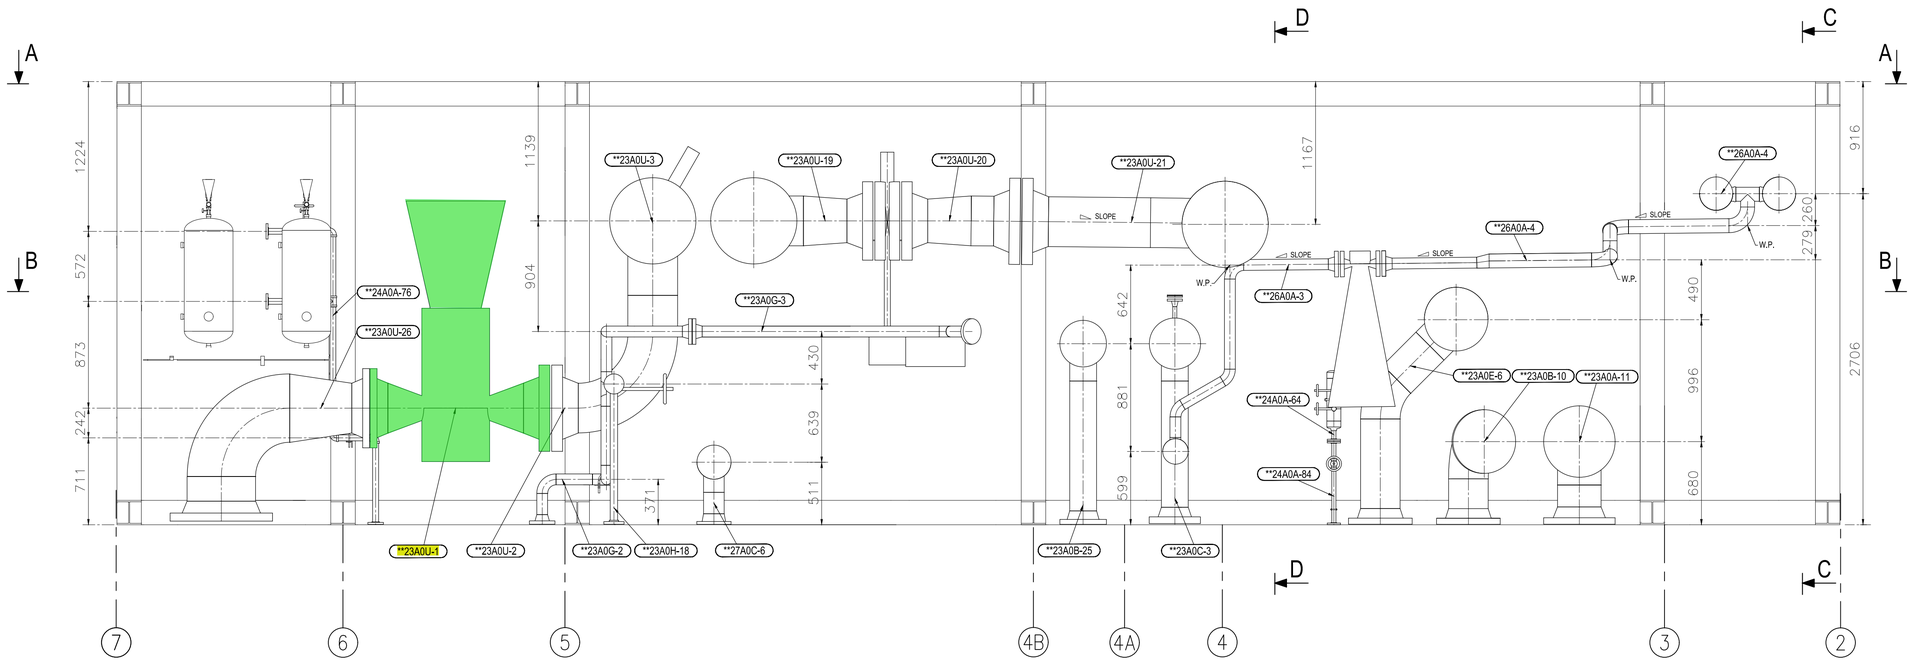

MD-3.1 ELEVATION VIEW
SECTION 'D-D'

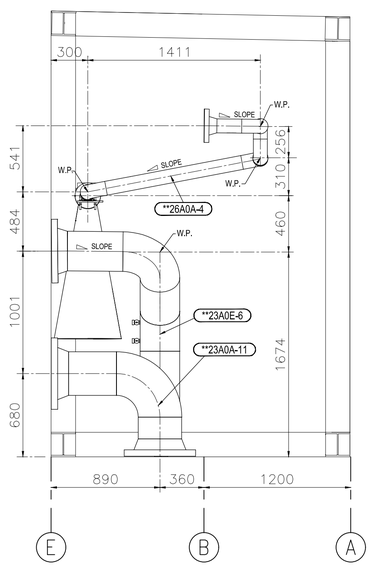

MD-3.1 SECTION 'C-C'
(LOOKING EAST)

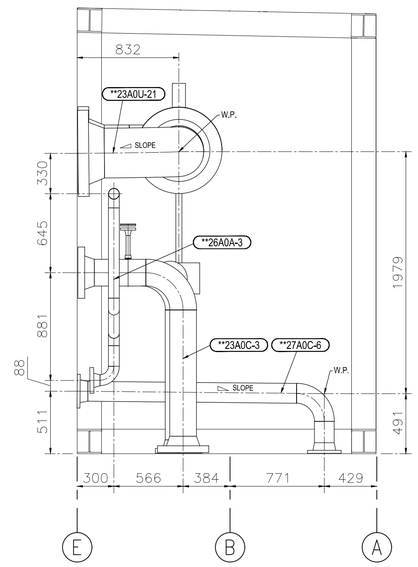

MD-3.1 SECTION 'D-D'
(LOOKING EAST)

REFERENCES

MDL ITEM #	MPWA MDL DESCRIPTION	DETAILS FOR
1	FOUNDATION PLAN AND SUMMARY LOADING DATA FOR MODULE GT ENCLOSURE	GENERAL LOCATION
20	GA DRAWING FOR MODULARIZED JAC GT ENCLOSURE	GENERAL LOCATION

NOTES

1. DIMENSIONS : MM [INCHES]
2. LABELING
   - ××XXXXXX ——PIPE LINE
   - (××XXX-X) ——SPOOL NO
3. SOME STRUCTURAL MEMBERS AND GRATINGS ARE HIDDEN FOR A MORE CLEAR VIEW WHERE IT IS CONSIDERED NECESSARY
4. WP : WORKING POINT FOR SLOPE LINE

REV.	DESCRIPTION	DATE	BY	CHECK	APPROVAL
0	ISSUED FOR CONSTRUCTION	01.MAY.2024	S.H.	M.F.	N.K.

This drawing is the property of Cimtas and all rights reserved

REVISIONS

CUSTOMER

PROPRIETARY AND CONFIDENTIAL:
This document contains Confidential and Proprietary information of Mitsubishi Power Americas, Inc. Neither this document, nor any information obtained therefrom is to be reproduced, transmitted or disclosed to any third party without first receiving the express written authorization of Mitsubishi Power Americas, Inc.
©2024 , Mitsubishi Power Americas, Inc.

MITSUBISHI POWER

CUSTOMER JOB NO: –

ITEM NO: MDL-150

DWG NAME: MD-3.1 PIPING SUPPORT & SPOOLS GENERAL ARRANGEMENTS DRAWINGS **(GA FOR SPOOLS)**

REF.DWG.NO.: –


PREPARED BY: cimtas


JOB NO	SHEET	SCALE	SIZE
2E00140	1/1	1/25	A1

DRAWING NO: 2E00140-PI-094-001-MD-3.1

REV.: 0

REVISION RECORD

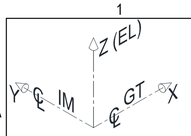

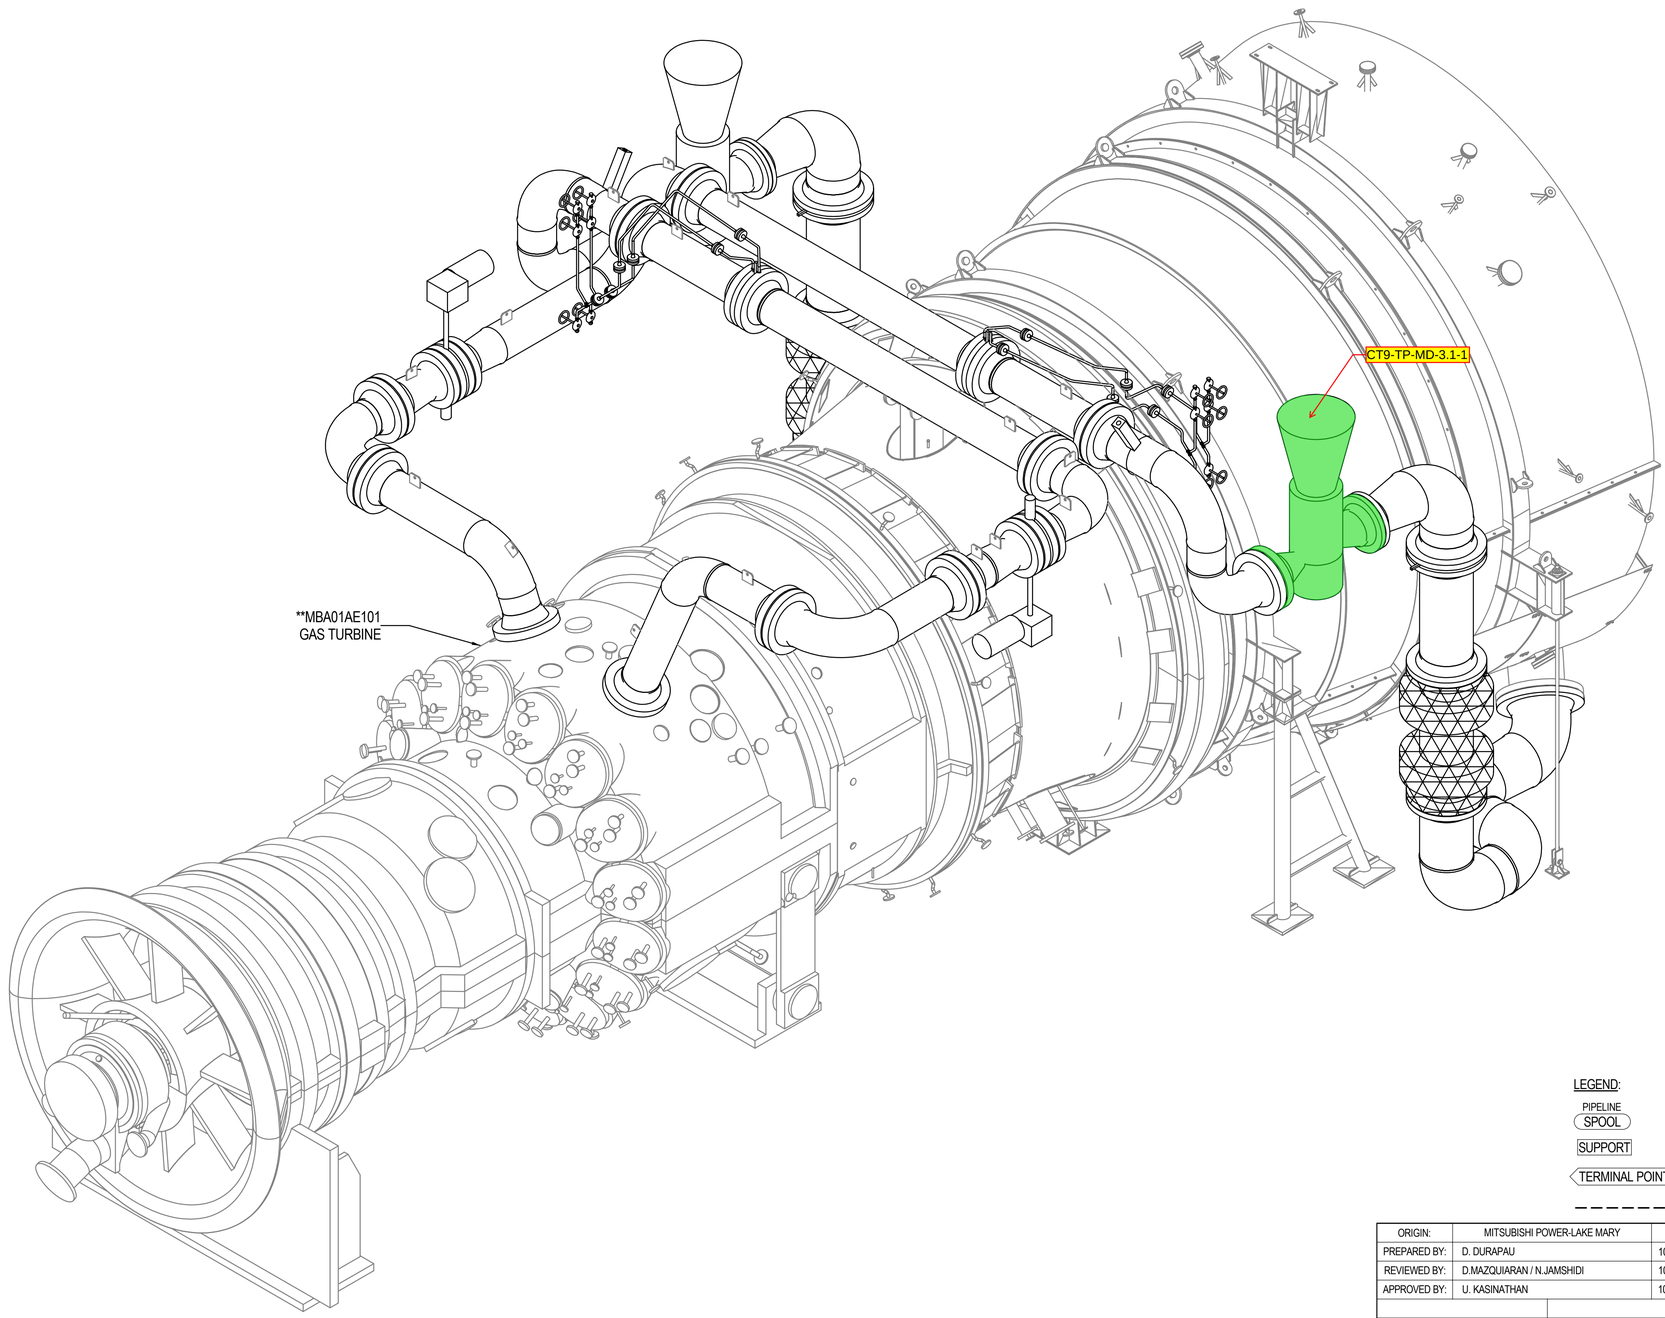

LEGEND:

PIPELINE / SPOOL	INDICATES PIPELINE ON THE TOP AND SPOOL ON THE BOTTOM.
SUPPORT	INDICATES SUPPORT.
TERMINAL POINT	INDICATES TERMINAL POINT.
– – – – – – –	INDICATES TRACING.

ORIGIN:	MITSUBISHI POWER-LAKE MARY	DATE:	MITSUBISHI POWER DRAWING NUMBER:	REV. NO.:	SYSTEM CODE:
PREPARED BY:	D. DURAPAU	10/22/2025	**N05-003545**	**0**	**23A0U**
REVIEWED BY:	D.MAZQUIARAN / N.JAMSHIDI	10/28/2025	**TURBINE BY-PASS PIPING**		
APPROVED BY:	U. KASINATHAN	10/31/2025	**INTERNAL TO GT PACKAGE**		
			FOR FABRICATION & ERECTION		
			N05-ISO-MBH-BR-AN		
			P&ID DRAWING NUMBER: N01-PID-MBH-00-02		
			M501JAC GAS TURBINE		
			PROJECT CODE: -	P&ID: -	
			PIPELINE: -	PAGE NUMBER: 1 OF 7	

PROPRIETARY AND CONFIDENTIAL:
This document contains Confidential and Proprietary information of Mitsubishi Power Americas, Inc. Neither this document, nor any information obtained therefrom is to be reproduced, transmitted or disclosed to any third party without first receiving the express written authorization of Mitsubishi Power Americas, Inc.
©2025 , Mitsubishi Power Americas, Inc.

MITSUBISHI POWER

EXPORT CONTROL DIVERSION WARNING
This document contains data which if exported from the United States must be exported in accordance with the export administration regulations, diversion contrary to U.S. law is prohibited.

ECCN: EAR99 No License Req'd


SIL2

MITSUBISHI POWER ENGINEERING
PLANT ENGINEERING

DEPARTMENT:
SECTION:

DRAWING DISTRIBUTION LIST

REVISION RECORD

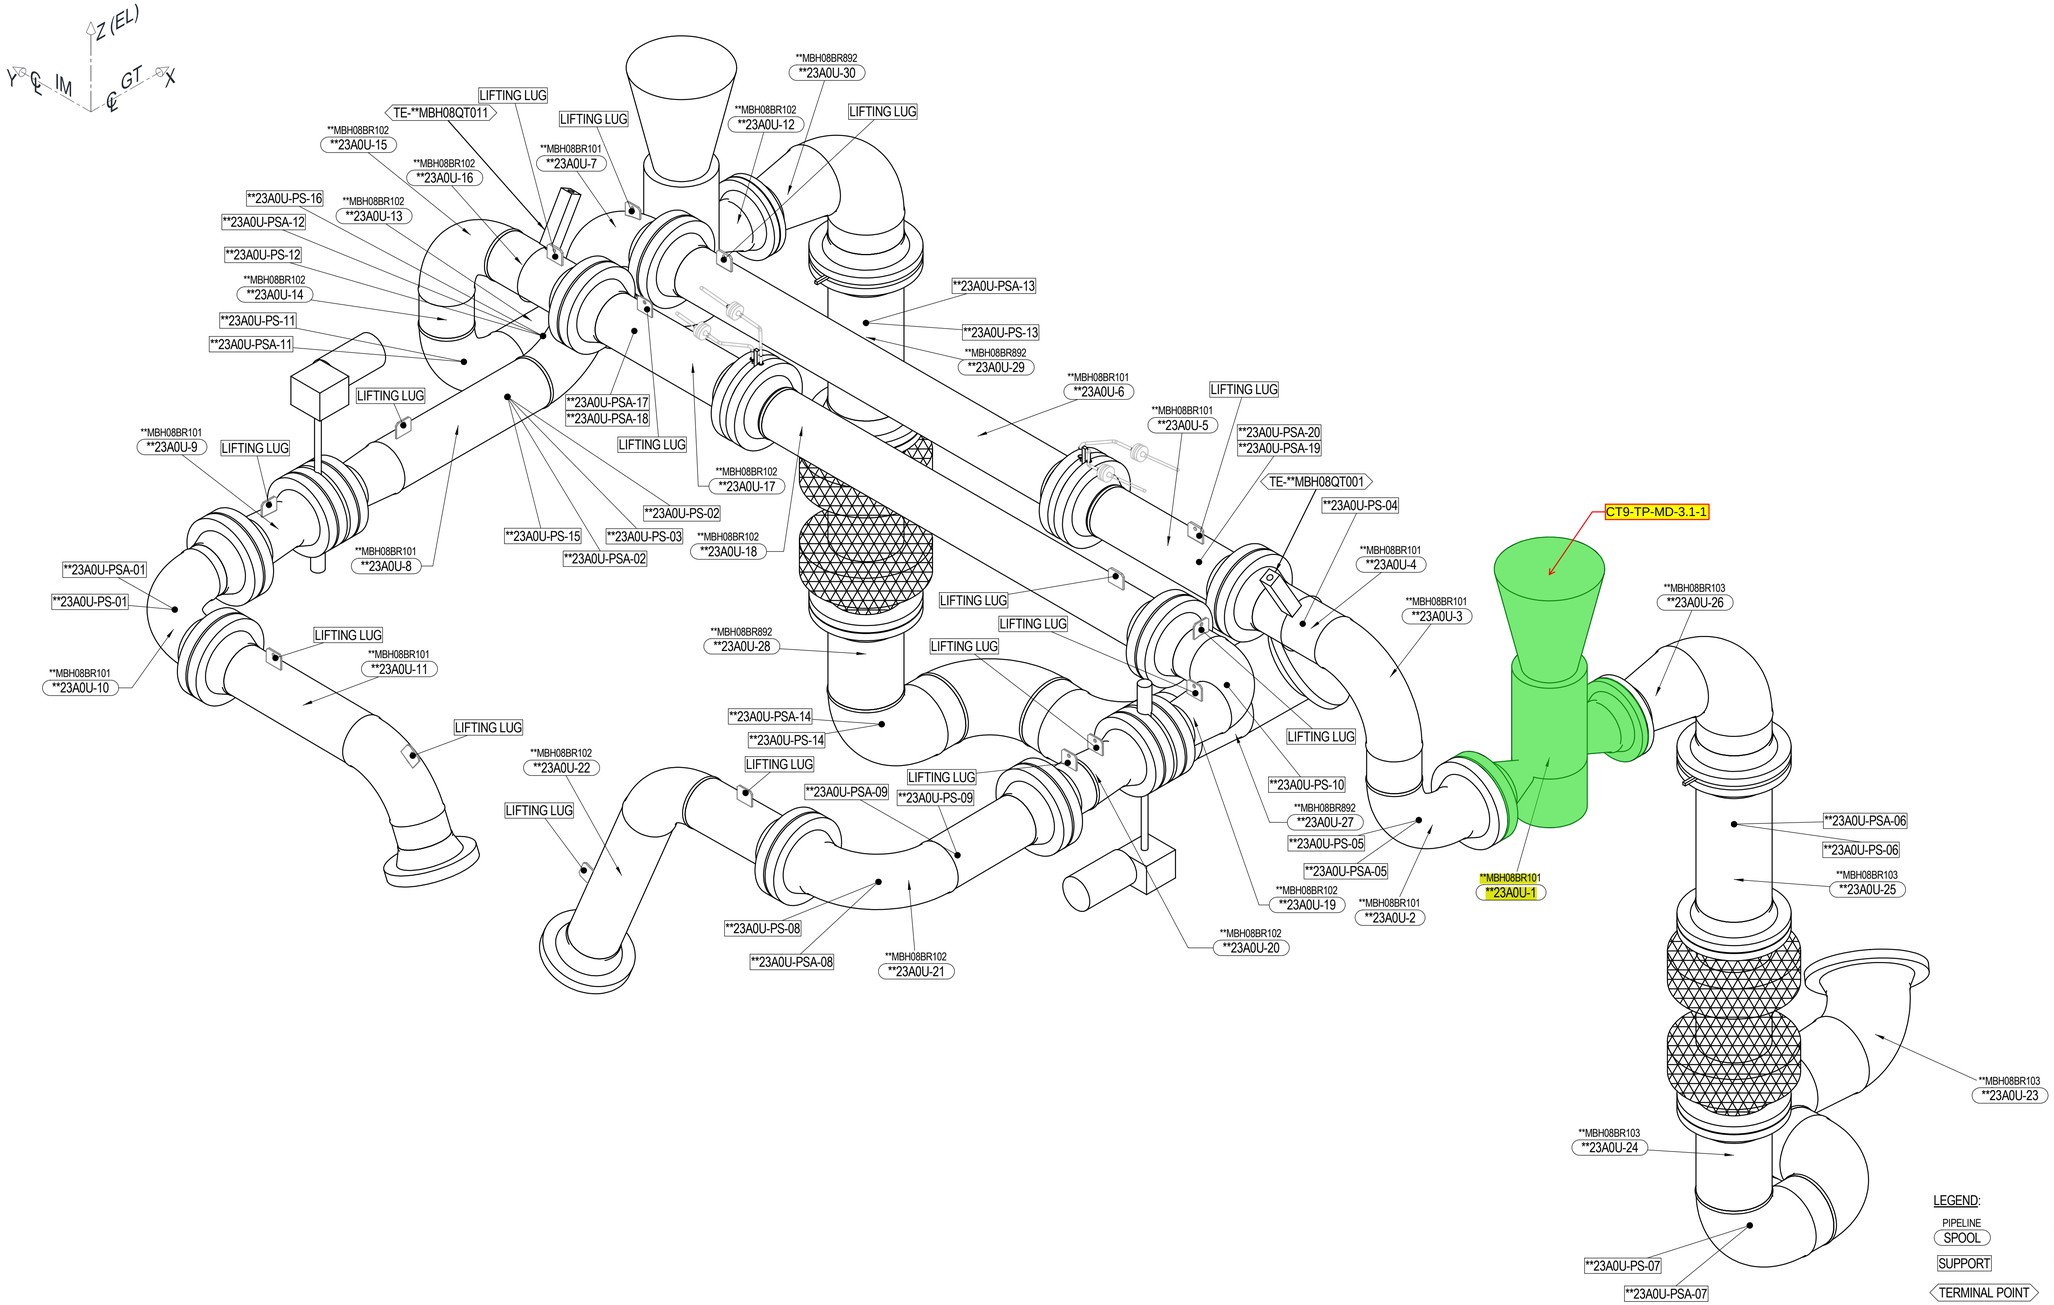

LEGEND:

PIPELINE SPOOL	INDICATES PIPELINE ON THE TOP AND SPOOL ON THE BOTTOM.
SUPPORT	INDICATES SUPPORT.
TERMINAL POINT	INDICATES TERMINAL POINT.
– – – – – – –	INDICATES TRACING.

ORIGIN:	MITSUBISHI POWER-LAKE MARY	DATE:	MITSUBISHI POWER DRAWING NUMBER:	REV. NO.:	SYSTEM CODE:
PREPARED BY:	D. DURAPAU	10/22/2025	**N05-003545**	**0**	**23A0U**
REVIEWED BY:	D.MAZQUIARAN / N.JAMSHIDI	10/28/2025	**TURBINE BY-PASS PIPING**		
APPROVED BY:	U. KASINATHAN	10/31/2025	**INTERNAL TO GT PACKAGE**		
			FOR FABRICATION & ERECTION		
			N05-ISO-MBH-BR-AN		
			P&ID DRAWING NUMBER: N01-PID-MBH-00-02		
			M501JAC GAS TURBINE		
PROJECT CODE:	-	P&ID:	-		
PIPELINE:	-	PAGE NUMBER:	4 OF 7		

PROPRIETARY AND CONFIDENTIAL:
This document contains Confidential and Proprietary information of Mitsubishi Power Americas, Inc. Neither this document, nor any information obtained therefrom is to be reproduced, transmitted or disclosed to any third party without first receiving the express written authorization of Mitsubishi Power Americas, Inc.
©2025 , Mitsubishi Power Americas, Inc.

MITSUBISHI POWER

EXPORT CONTROL DIVERSION WARNING
This document contains data which if exported from the United States must be exported in accordance with the export administration regulations, diversion contrary to U.S. law is prohibited.


ECCN: EAR99 No License Req'd

SL2

MITSUBISHI POWER ENGINEERING
PLANT ENGINEERING

DEPARTMENT:
SECTION:

DRAWING DISTRIBUTION LIST

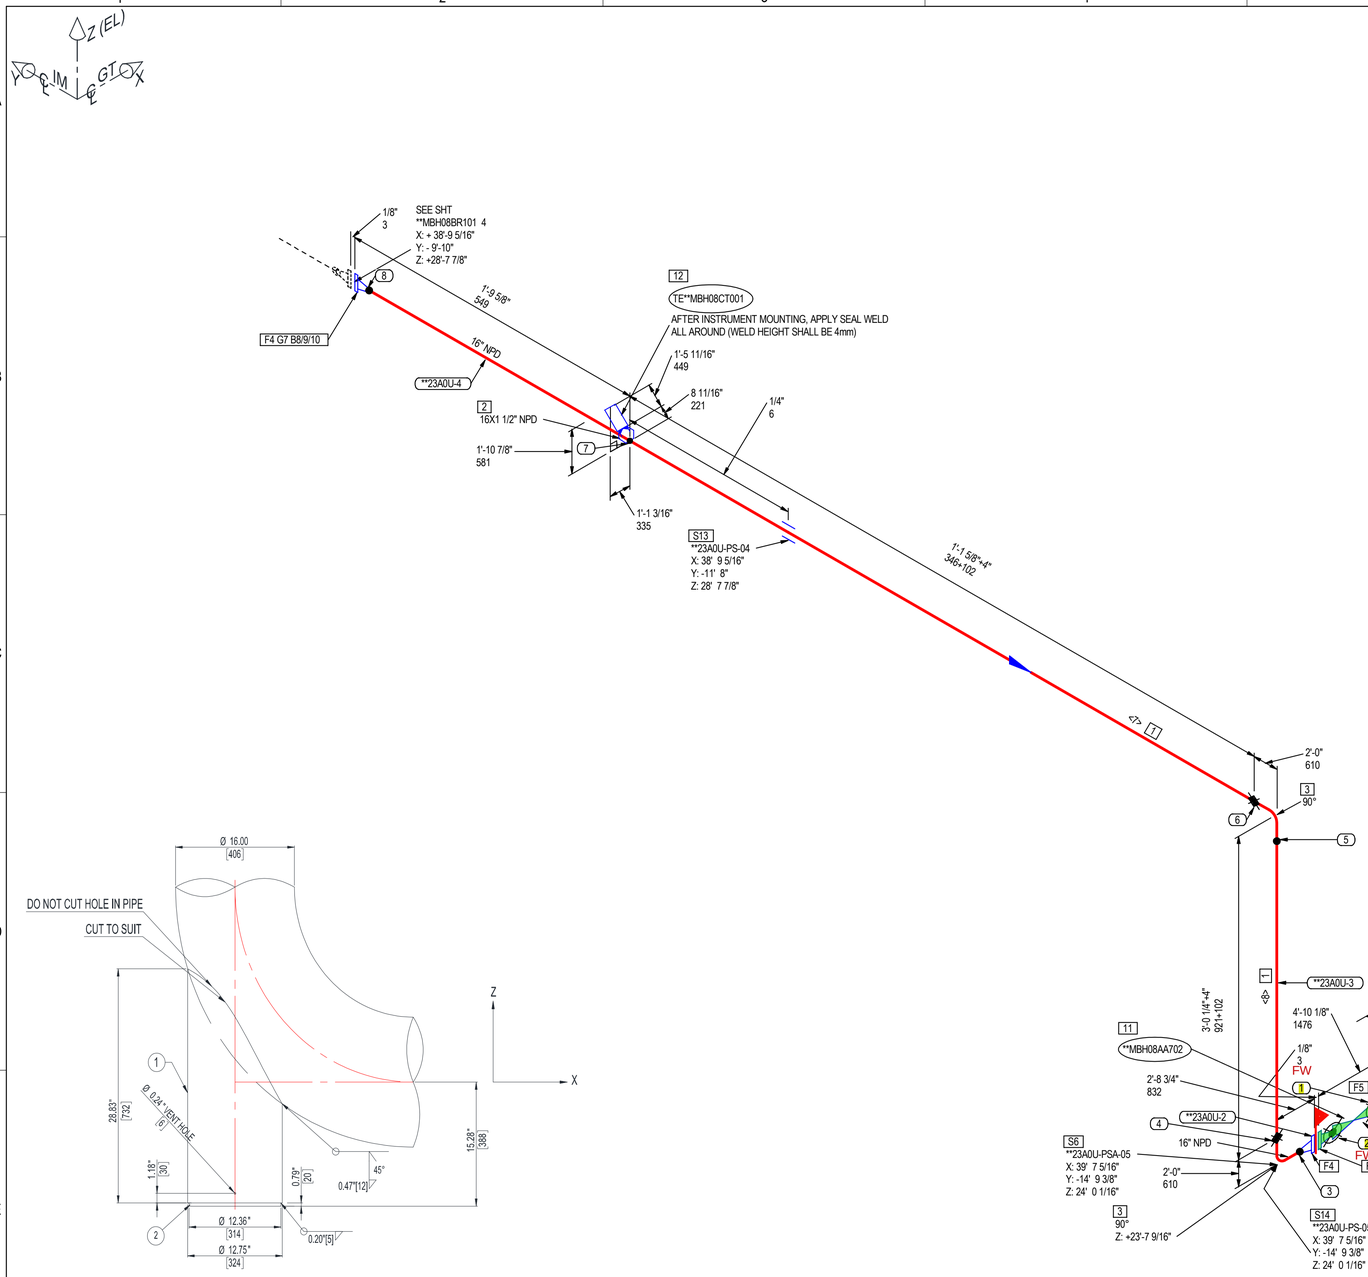

DETAIL - PIPE SUPPORT ATTACHMENT
[**23A0U-PSA-05]
1- PIPE 12", SCH 80, ASTM A335-P22, SEAMLESS L= 28.83", 1 PIECE
2- PLATE ASTM A36, Ø12.336" x thk. 0.79", 1 PIECE

NOTES:
1. WELDING AT PIPES MARKED WITH ✂ SHALL BE ADJUSTED AT SHOP TO FIT DURING JIG ASSEMBLY. THE MARK ✂ ON THE DRAWING INDICATES AN EXCESS LENGTH OF 4" (100mm) ADDED TO THE PIPE FOR ADJUSTED DURING ASSEMBLY.
2. WELDING AT PIPES MARKED WITH ⊗ SHALL BE ADJUSTED AT SHOP TO FIT DURING ASSEMBLY.

SHOP MATERIALS - FABRICATION ONLY

PT NO	DESCRIPTION	NPD (IN)	CMDTY CODE	QTY
1	PIPE, S-80, BE, ASME B36.10M, ASTM A335-P22, SEAMLESS	16	MPAAZZBOZZABAAIJ	4.0'
2	THREDOLET, CL3000, FTE, MSS-SP-97, ASTM A182-F22-CL 3	16X1 1/2	MMEMAWBUZZGKGAGJ	1
3	90 DEG ELBOW LR, S-80, BE, ASME B16.9, ASTM A234-WP22-CL 1, SEAMLESS	16	MMCMZZBOZZAAEAHK	2
4	FLANGE WN, CL900, RFFE x BE, ASME B16.5, ASTM A182-F22-CL 3, S-80 bore	16	MFAAARDCZZAADAGJ	3
5	FLANGE WN, CL300, RFFE x BE, ASME B16.5, ASTM A182-F22-CL 3, S-40 bore	16	MFAAAMDCZZAADAGJ	1
	PIPE SUPPORTS			
6	PIPE SUPPORT ATTACHMENT (REFER TO DETAIL)	16	**23A0U-PSA-05	1

OTHER THAN SHOP MATERIALS - ERECTION ONLY

PT NO	DESCRIPTION	NPD (IN)	CMDTY CODE	QTY
7	GASKET, SPIRAL WOUND, CL900, 0.175" THK, ASME B16.20, WINDING INCONEL X750HT/FILLER THERMICULITE 835, INNER RING 316L/CENTERING RING 316	16	MDARAXAAKXAKUS	2
8	STUD, CONTINUOUS THREAD, ASME B18.31.2, ASTM A193-B16, 8-UN - 12.5 in. Length	1 5/8	MBAZZALZZIAGBFXZ	40
9	NUT, HEAVY HEX, ASME B18.2.2, ASTM A194-7, 8-UN	1 5/8	MNOZZALAAZPCEAKU	80
10	WASHER, SPECIAL SHAPED LOCK, 16in NPD, 2.0mm THK, MHPSA G1-90945, ASTM A240-304	1 5/8	MWQZZZZBBIBEAMDP	80
	INSTRUMENTS			
11	GT TURBINE BYPASS VALVE (A) CL900xCL300, RF, **MBH08AA702	16		1
12	GT TURBINE BYPASS (A) TEMPERATURE, TE**MBH08CT001	1 1/2		1
	PIPE SUPPORTS			
13	PIPE SUPPORT	16	**23A0U-PS-04	1
14	PIPE SUPPORT	16	**23A0U-PS-05	1
	SPOOLS			
	**23A0U-1, **23A0U-2, **23A0U-3, **23A0U-4			

CUT PIPE LENGTH

PIECE NO	LENGTH (FT-INS)	NPD (IN)	REMARKS	END ONE	END TWO	ITEM CODE
<7>	2'6 9/16"	16		BEVEL	BEVEL	MPAAZZBOZZABAAIJ
<8>	1'4 1/4"	16		BEVEL	BEVEL	MPAAZZBOZZABAAIJ

ACTUAL QUANTITY OF WASHERS SHALL BE CONSIDERED AS HALF OF THE QUANTITY SHOWN ON ISOMETRICS

NOTES:
1. THE X AND Y COORDINATES ARE WITH RESPECT TO THE INTERSECTION OF THE CENTERLINE OF THE GAS TURBINE (GT) AND THE INLET MANIFOLD (IM). THE Z (EL) COORDINATE IS WITH RESPECT TO THE TOP OF CONCRETE, WHICH IS 15'-9" [4800 mm] BELOW THE CENTERLINE OF THE GT AND IS 0'-0".
2. ALL PIPE SUPPORT COORDINATES ARE WITH RESPECT TO THE CENTERLINE OF THE INSTALLED SUPPORTED PIPE.
3. THE MARK 'FFW' (FIELD FIT WELD) IN THE DRAWING INDICATES EXCESS LENGTH OF APPROX. 4 INCHES IDENTIFIED AS LOOSE IN THE DRAWING TO BE CUT AND ADJUSTED AT THE FIELD.
4. ALL WELDING TO BE DONE AND INSPECTED PER LATEST APPLICABLE EDITION OF ASME B31.1 AND SECTION IX AVAILABLE ON THE PROJECT AWARD DATE.
5. PIPING SHALL BE INSTALLED PER THE INDICATED SLOPE.
6. FOR ANY FURTHER INFORMATION REQUIRED DURING INSTALLATION, CONSULT MITSUBISHI POWER TFA (TECHNICAL FIELD ADVISOR) AT SITE.
7. ⟨XXX## ###⟩ INDICATES PIPING TERMINAL POINT.

WELD NO	WELD TYPE	WELD CAT	NPD	QTY
8	BW	S	16"	1
7	LET	S	1 1/2"	1
6	BW	S	16"	1
5	BW	S	16"	1
4	BW	S	16"	1
3	BW	S	16"	1
2	BW	S	16"	1
1	BW	S	16"	1

PIPING SPEC:	ADC	PAINTING SPEC: PER PROJECT SPECIFICATION	
FLUID CODE:	AC, GT COMPRESSED AIR	INTERIOR SURFACE TREATMENT SPEC: LU-00129	
MAX. PRESS.:	428.00 psig / 2.95 MPag		
TEST PRESS.:	642.00 psig / 4.43 MPag		
MAX. TEMP:	1040 F / 560 C		
INSULATION SPEC:	LU-00331		

REV. #	DESCRIPTION	BY	CHK	APP	DATE
	REVISION RECORD				

WELD TYPE IDENTIFIER:
BW - BUTT WELD
SW - SOCKET WELD
SOF - SLIP-ON FLANGE
SOB - SET-ON BRANCH
LET - OLET, LATROLET OR HALF COUPLING
TW - TACK WELD
MW - MITER WELD

WELD CATEGORY IDENTIFICATION:
● S - SHOP
⊗ FW - FIELD WELD
⊗ FFW - FIELD FIT WELD

SYMBOLOGY:
WELD NUMBER
PART NUMBER (PT NO)
< > CUT LIST PIECE NUMBER

SYMBOL IDENTIFIER:
F - FLANGE
G - GASKET
B - BOLT
N - NUT
W - WASHER
O - O-RING
L - LOCK WIRE

PROPRIETARY AND CONFIDENTIAL:
This document contains Confidential and Proprietary information of Mitsubishi Power Americas, Inc. Neither this document, nor any information obtained therefrom is to be reproduced, transmitted or disclosed to any third party without first receiving the express written authorization of Mitsubishi Power Americas, Inc.
©2025 , Mitsubishi Power Americas, Inc.

MITSUBISHI POWER

ORIGIN:	MITSUBISHI POWER-LAKE MARY	DATE:	MITSUBISHI POWER DRAWING NUMBER:	REV. NO.:	SYSTEM CODE:
PREPARED BY:	D. DURAPAU	10/22/2025	N05-003545	0	23A0U
REVIEWED BY:	D.MAZQUIARAN / N.JAMSHIDI	10/28/2025	TURBINE BY-PASS PIPING		
APPROVED BY:	U. KASINATHAN	10/31/2025	INTERNAL TO GT PACKAGE		
			FOR FABRICATION & ERECTION		
			N05-ISO-MBH-BR-AN		
			P&ID DRAWING NUMBER:N01-PID-MBH-00-02		
			M501JAC GAS TURBINE		
PROJECT CODE:	-	P&ID:	-		
PIPELINE:	**MBH08BR101	PAGE NUMBER:	5 OF 5		

EXPORT CONTROL DIVERSION WARNING
This document contains data which if exported from the United States must be exported in accordance with the export administration regulations, diversion contrary to U.S. law is prohibited.

ECCN: EAR99 No License Req'd
SL2
MITSUBISHI POWER ENGINEERING
PLANT ENGINEERING
DEPARTMENT:
SECTION:
DRAWING DISTRIBUTION LIST